Bodentanks			Bestückung																
	Typ	Abmessungen	Elektrotechnik								A/V-Technik							TGA	
			Starkstrom							Schwachstrom								Wasser	Abwasser
				Schuko	CEE	Doppel-LAN	LWL-Duplex			Starkstrom		SDI	LWL-Duplex	V-LAN	A-LAN	Intercom-LAN	Frei-LAN		
Nr.	TK	B x L	Schuko	EDV	16A	2x RJ45	2x LC	HDMI		Schuko	XLR	BNC	2x LC	RJ-45	RJ-45	RJ-45	RJ-45	DN 15	Stutzen (139,5mm)
1	A/Kubus	300 x 300				1													
1	A/Foyer	300 x 300	2			1													
1	A/Büro	300 x 300	2			1													
2	B									2	4	2	4	3	2	0	2		
	C/Foyer		5		1													1	1
3	C/Kubus	600 x 600	5		1													1	1
4	D	300 x 300	2				2				2		2						
5	E									2	4	2	4	2	2	0	2		
6	F									3	8	4	8	8	2	2	4		
7	G																		
8	H	500 x 500								3	6	2	4	4	2	2	2		
9	I									2	2	0	2	0	0	0	0		
10	J	300 x 300								0	2	0	0	0	0	0	2		
11	K	500 x 500	2			1													
12	Z41	300 x 300																	
13	Z42	300 x 300																	
14	Z43	400 x 400																	
15	L	264 x 264	2	2		2													
16	M	264 x 264	2	2		2		1											
17	N	264 x 264																	

Zugangskontrolleinrgen

- AC Accesomanager
- V1 Verteiler
- RLL Raumtreue Erkennung
- ZKA Zugangskontrolle
- Kartenleser
- ZKA1 Zerge Typ 3004
- ZKA2 Wand Typ 3000
- ZKA3 Integriert Typ 3000
- DK Ansteuerung über ZKA
- ZM Zutrittsmanager
- I/O Modul

Digitale Schließanlage

- Wireless Gateway
- Dig. Zylinder "Cwiss"
- Hebzylinder Standard (gegenüber Drehknopf)
- Hebzylinder ohne Gegenstück
- Zylinder Dual 2 Richtungen / Durchgang
- Hebzylinder (Einbau in FTS)
- Übergabepunkt Türfeschnik oder Fensterfeschnik

Raumüberwachungssensoren

- Kamera
- Kamera Schwenk
- Kamera Video Dome
- Aussenwärmebildkamera mit Wandhaltung, Wetterschutzgehäuse und Scheibenheizung
- Innenkamera
- Kameramast
- Monitor
- Video Aufzeichnung
- Video-Zentrale
- Video-Unter-Zentrale

Einbruchmeldesensoren

- EMZ Einbruchmeldezentrale
- ÜGP Übertragungsgerät
- AT Anzeiger-/Bedienfeldbeleu
- AT Anzeigefeldbeleu
- Bus-Koppler
- Aussendarmierung optisch + akustisch
- Aussensirene
- Innensirene
- Lesegerät
- Lesegerät + Codeeingabe
- Wärmefühler
- Bewegung (Anbindung)
- Schaltvorrichtung Schlüssel
- Sperrelement
- Riegelschaltkontakt
- Magnetkontakt
- Glasbruchmelder passiv
- Glasbruchmelder aktiv
- Infrarot-Bewegungsmelder
- Infrarot-Rundummelder 360
- Zwalmelder
- Koppler
- Körperschallmelder
- Überfallmelder
- Flächenüberwachung z.B.: Folie, Draht, Alarmmatte
- Alarmgiss
- Verteiler
- Verteiler mit Tabbtogekontakt
- Auswertereinheit
- Wetterstrahlb-Tür

Brandmeldesensoren

- Druckknopfmelder
- Rauchmelder, optisch
- Thermodifferenzialmelder
- Multisensormelder optisch/thermisch
- Multisensormelder optisch/thermisch mit Akustik
- Multisensormelder opt./therm./Gas
- Melder für Lüftungskanäle
- Linienförmiger Rauchmelder Empfänger
- Linienförmiger Rauchmelder Sender
- Weiterporaldeiranzeige
- Signalgeber, akustisch
- Blitzleuchte
- Kontrolleinheit
- Bus Koppler
- Hauptmelder
- Fw-Informations-Beden-System
- Freischaltelement
- Feuerwehr-Schlüsselkepot
- Übertragungseinrichtung Fw
- Loggeplanltableau
- Brandmeldezentrale
- Übertragungsgerät
- Anzeigefeldbeleu
- Abgesetztes Bedienfeld
- Netzgerät
- Revisionsöffnung >= 40x40cm
- Revisionsöffnung >= 30x60cm

Tiefergängungen zu DIN8

- c im Kanal
- im Doppelboden
- in Zwischendecke
- mit Signalmelder im Sockel
- Explosionsgeschützt

- 1 30cm mittig über OK Tür
- 2 30cm mittig über OK Tür
- 3 30cm unterhalb Decke
- 4 30cm unterhalb Abhangdecke
- 5 Anbau an Decke (Aufbau)

Kennzeichnung Brandmeldesensoren

- Melder-Nr.
- Meldergruppe Nr.
- Loop-Nr.

- RAS Anzeigeöffnung Zwischendecke
- RAS Rotor Zwischendecke
- RAS Anzeigeöffnung Decke
- RAS Rotor Decke
- RAS Auswertereinheit
- LWM-Filterrotor
- LWM-Auswertereinheit

Die Konformität der Bauteile nach DIN EN 54 sowie der Systemkonformität der BMA-Komponenten nach DIN EN 54/13 sind zu gewährleisten !

SAA

- 1 Lautsprecher SAA
- 2 LV Pos.5.2.1.20
- 3 LV Pos.5.2.1.21
- 4 LV Pos.5.2.1.22
- 5 LV Pos.5.2.1.23
- 6 LV Pos.5.2.1.25
- 7 LV Pos.5.2.1.26
- 8 LV Pos.5.2.1.27
- 9 LV Pos.5.2.1.28

Türsprech-/Türöffneranlagen

- Türsprech-Videotableau
- Türsprech-Tableau
- Sprechstelle innen
- Sprechstelle innen System-Telefon
- Sprechstelle innen Video
- Klingeltaster
- Rufentzergerät
- Läutwerk
- Türöffner

Lichtruf

- Notruf-Signalleuchte
- Ruf-/Abbeltaster
- Zugtaster mit Schnur
- Zimmerterminal mit Display
- Netzgerätt USV
- I_O Modul
- Systemswitch

Übertragungstechnik

- Anschlussdose 1x/2x RJ45 Cat 6
- Festanschluss Cat 6
- Anschlussdose 2x UML
- ZDV-Etagenverteiler
- ZDV-Rangierverteiler
- Verteilerschrank 19"
- Wireless LAN Sender-/Empfangsstation
- DECT Sender-/Empfangsstation
- VGA-Verbindungsdose
- HDMI-Verbindungsdose
- Audio-Verbindungsdose

Kennzeichnung ZDV-Anlage

- Patchfeld-Nr.
- Verteiler-Nr.

* = Ausstattung nach Vorgabe ELT nicht übereinstimmend mit Türliste Architekt Türdetail stimmt nicht!!! Klärung mit AG-Planern erforderlich

Grundkonzeption BOS-Gebäudefunk zur Zeit in Bearbeitung keine LP-5 vorhanden.

zur Zeit ausstehend Vorgaben der LP-5 zur Anbindung Türen/ RVA/ Entrauchung an die zentrale "Türsteuerung".

SAA-Hinweis: Die Lautsprecherbyzen nach Vorgabe LP-5 und LV sind nicht eindeutig zu zuordnen Klärung erforderlich!

Sprachformanlagen

- Anrufe Taster oben
- Antenne
- Ton Eingang
- SAA Zentrale
- SAA Unterzentrale
- Festanschluss Lautsprecher
- Festanschluss Notruf
- Lautsprecher Anschlusspunkt
- Lautsprecher Anschlussdose
- Lautsprecher
- Lautstärke ELA
- Lautstärke Regler PFL-Relais
- Wiesfon SAA
- Sprechstelle SAA

Kennzeichnung Sprachdarmanlagen

- Bld. Nr.
- Linien-Nr.

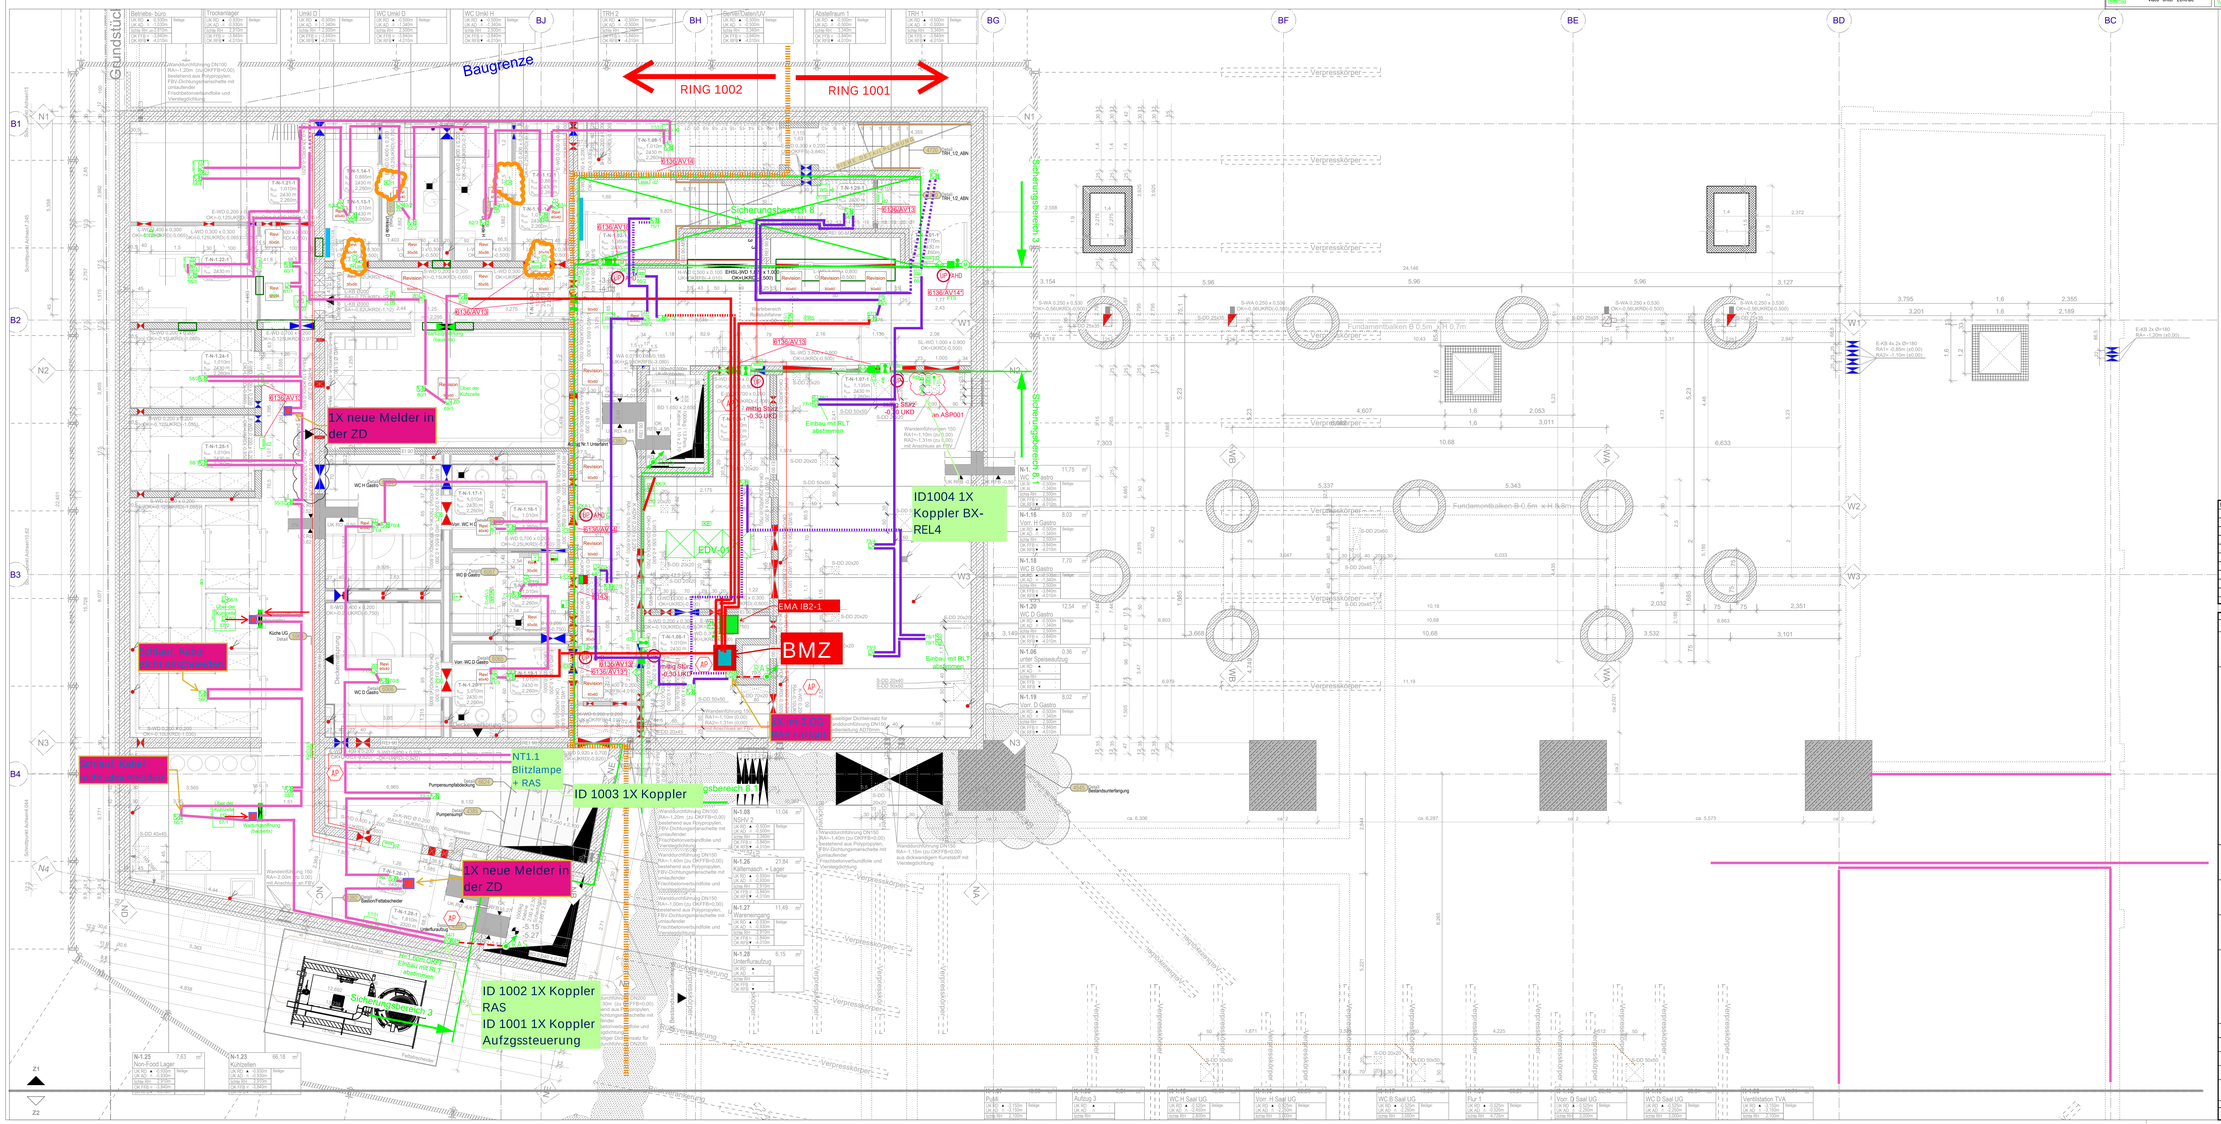

Index	Datum	Ges.	Änderung
			Index J.Rehms Gebäudetechnik GmbH
P02	14.11.24	PW	Einarbeitung der Freigaben B&K

Projektnummer	Gewerk	LFH	Planart	Ebene	Bauabschnitt	Freifeld	Index
K714	FIT	08	GR	UG	Z1	1001	P02

Basispläne:

Architektur: ARCHITEKTUR
Ausführung: AUSFÜHRUNG
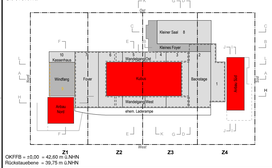
Übersicht: