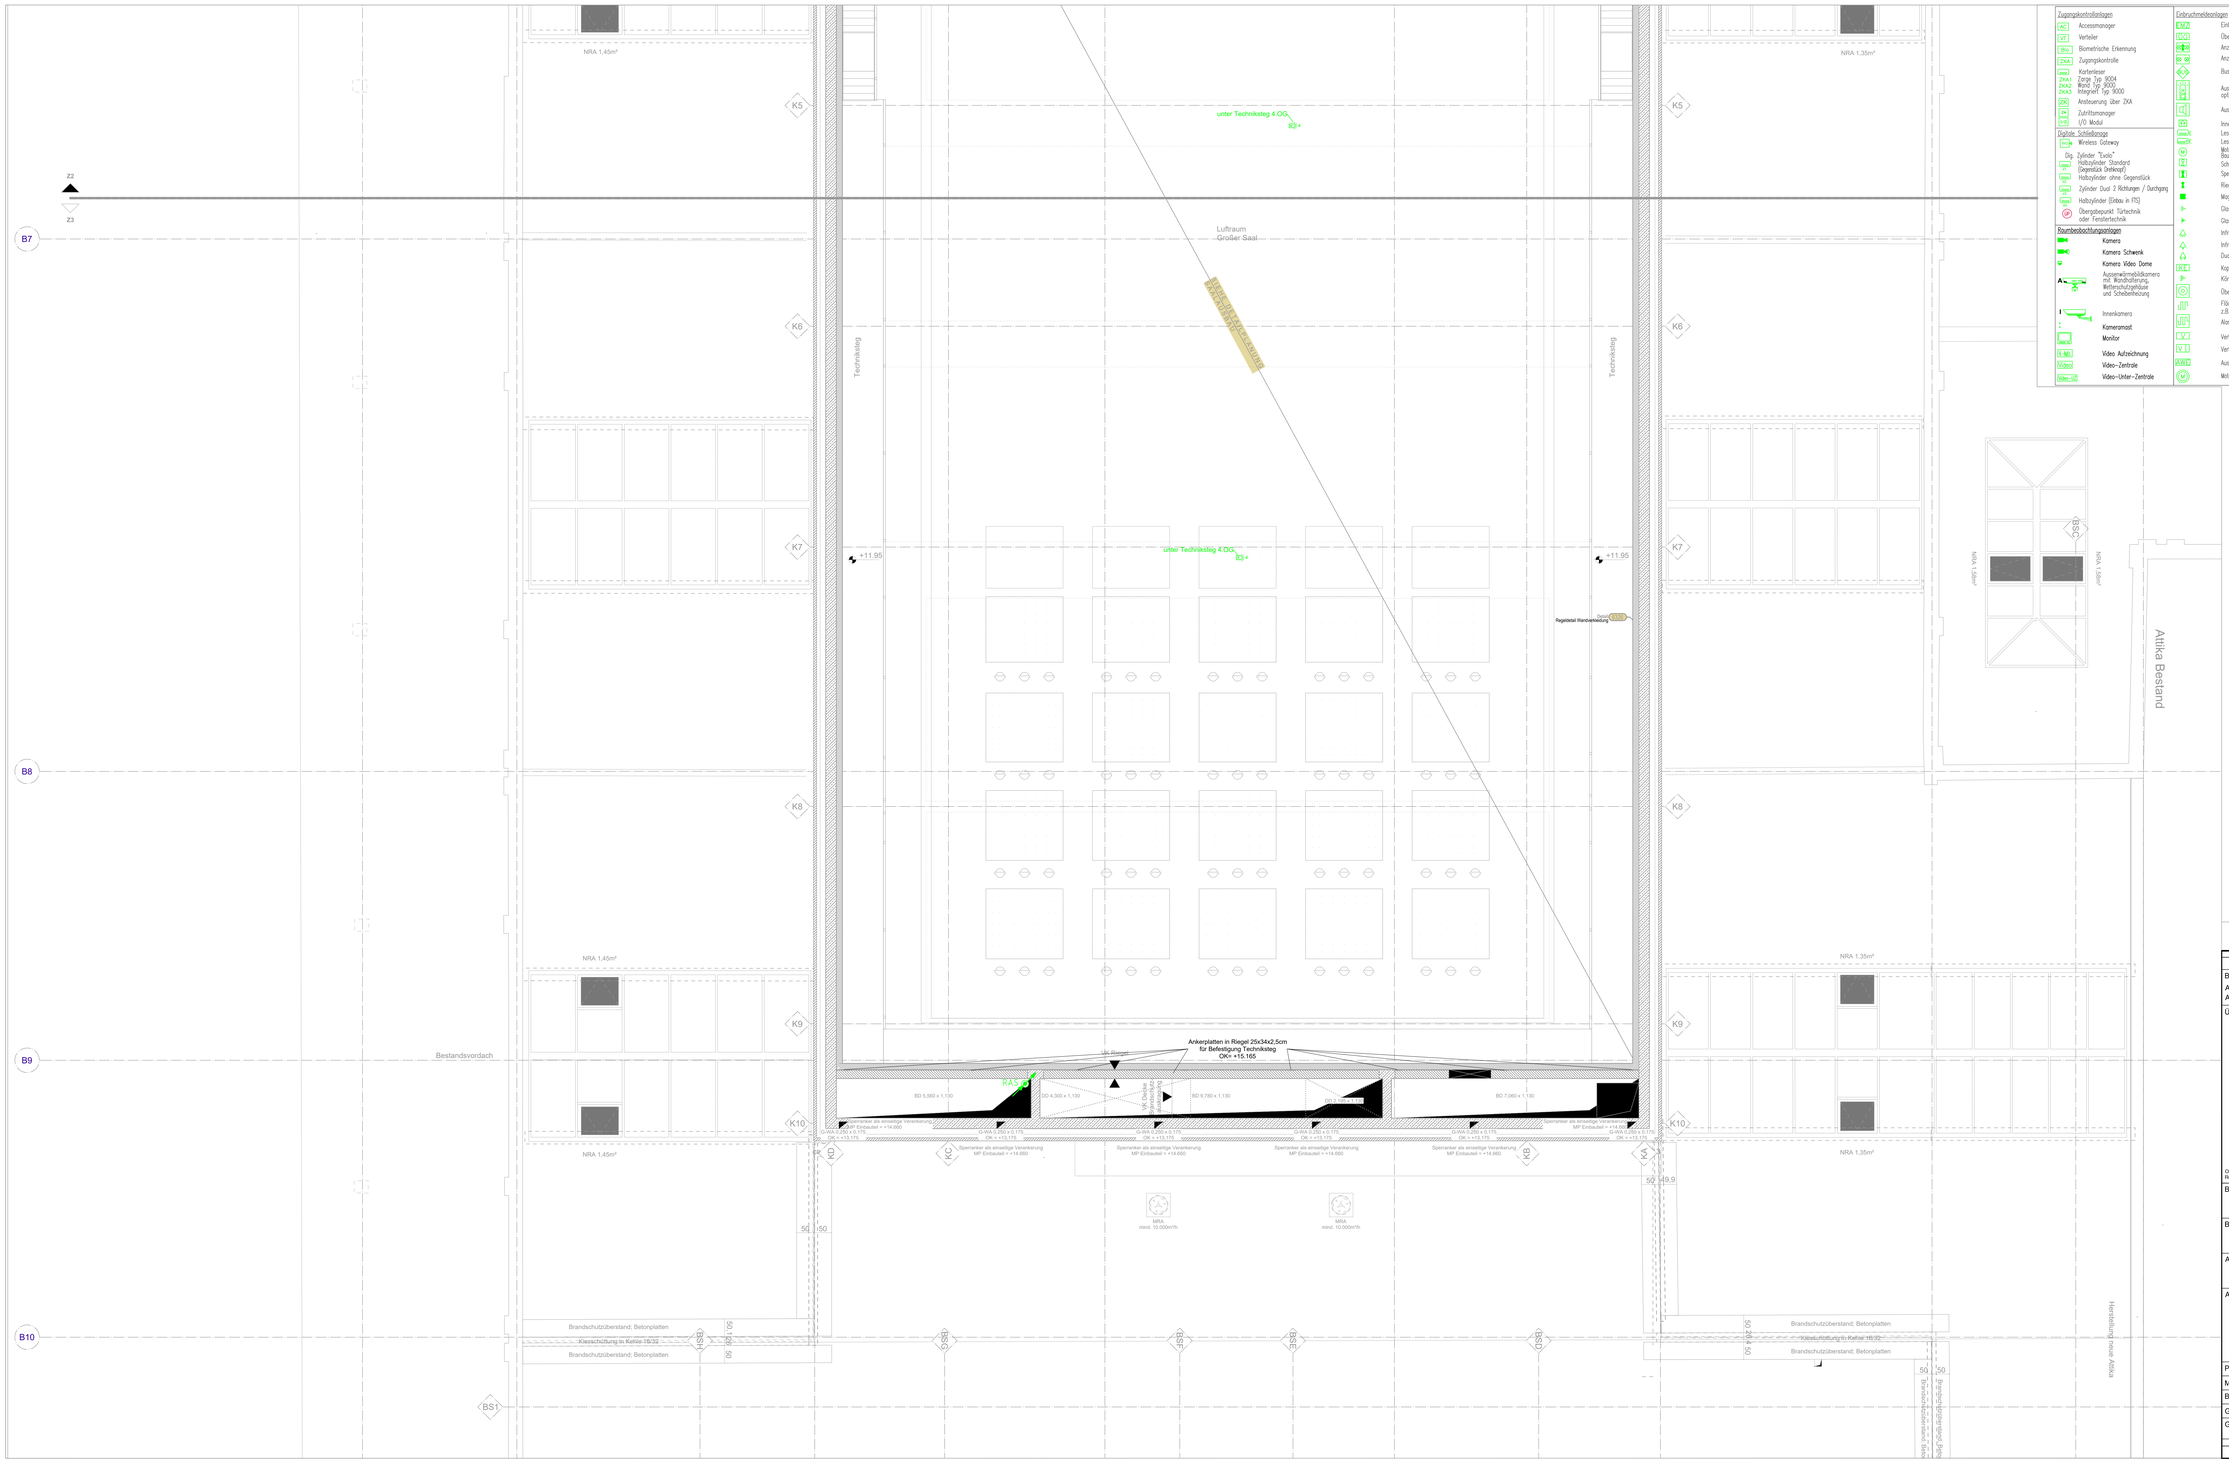

Zugangskontrollanlagen

- AC Accessmanager
- VT Verteiler
- Bio Biometrische Erkennung
- ZKA Zugangskontrolle
- Leser Kartenleser
  - ZKA1 Lesegerät Typ 9004
  - ZKA2 Wand Typ 9000
  - ZKA3 Integriert Typ 9000
- ZK Anstrauerung über ZKA
- ZP Zutrittsmanager
- I/O I/O Modul

Digitale Schließanlage

- Gw Wireless Gateway
- Dig. Zylinder "Evolo"
  - Halbzylinder Standard (Segmtück Defekt)
  - Halbzylinder ohne Gegenstück
  - Zylinder Dual 2 Richtungen / Durchgang
  - Halbzylinder (Erbau in FS)
  - ÜP Übergabepunkt Türtechnik oder Fenstertechnik

Raumüberwachungsanlagen

- Kamera
- Kamera Schwenk
- Kamera Video Dome
- Außenwärmebildkamera mit Blendfallerung, Wetterschutzgehäuse und Scheibenheizung
- Innenkamera
- Kameramast
- Monitor
- V.-Aufz. Video Aufzeichnung
- V.-Zentr. Video-Zentrale
- V.-Unter-Z. Video-Unter-Zentrale

Einbruchmeldeanlagen

- EMZ Einbruchmeldezentrale
- ÜG Übertragungsgerät
- Anzeige-/Bedientableau
- Anzeigetableau
- Bus-Koppler
- Aussenalarmierung optisch + akustisch
- Aussensirene
- Innensirene
- Lesegerät
- Lesegerät + Codeeingabe
- Motorschloss Baustellen (Abklemung)
- Schaltvorrichtung Schlüssel
- Sperrelement
- Riegelschaltkontakt
- Magnetkontakt
- Glasbruchmelder passiv
- Glasbruchmelder aktiv
- Infrarot-Bewegungsmelder
- Infrarot-Rundummelder 360
- Duelmelder
- Freischaltelement
- Feuerwehr-Schlüsseldepot
- Übertragungseinrichtung Fw
- Lageplantableau
- Brandmeldezentrale
- Übertragungsgerät
- Anzeigetableau
- Abgesetztes Bedienfeld
- Netzgerät
- Revisionsöffnung >= 40x40cm
- Revisionsöffnung >= 60x60cm

Textergänzungen zu BMA

- x im Kanal
- DB im Doppelboden
- ZD in Zwischendecke
- H mit Signalmelder im Sockel
- Ex Explosionsgeschützt

1. 30cm mittig über OK Tür
2. 30cm mittig über OK Tür
3. 30cm unterhalb Decke
4. 30cm unterhalb Abhangdecke
5. Anbau an Decke (Aufbau)

Kennzeichnung Brandmeldeanlage

0/2/3 Melder-Nr.
- Meldergruppe Nr.
- Loop-Nr.

- RAS Anzuqöffnung Zwischendecke
- RAS Rohr Zwischendecke
- RAS Anzuqöffnung Decke
- RAS Rohr Decke
- RAS RAS Auswerteeinheit
- LWM-Fühlerrohr
- LWU LWM-Auswerteeinheit

Die Konformität der Bauteile nach DIN EN 54 sowie die Systemkonformität der BMA-Komponenten nach DIN EN 54/13 sind zu gewährleisten !

Brandmeldeanlagen

- Druckknopfmelder
- Rauchmelder, optisch
- Thermodifferentialmelder
- Multisensormelder optisch/thermisch
- Multisensormelder optisch/thermisch mit Akustik
- Multisensormelder opt./therm./Gas)
- Melder für Lüftungskanäle
- Linienförmiger Rauchmelder Empfänger
- Linienförmiger Rauchmelder Sender
- Melderparallelanzeige
- Signalgeber, akustisch
- Blitzleuchte
- Kontrolleinheit
- Bus Koppler
- Hauptmelder
- Fw-Informations-Bedien-System
- Freischaltelement
- FSE Feuerwehr-Schlüsseldepot
- ÜE Übertragungseinrichtung Fw
- LPT Lageplantableau
- BMZ Brandmeldezentrale
- ÜG Übertragungsgerät
- AT Anzeigetableau
- ABF Abgesetztes Bedienfeld
- Netzgerät
- Revisionsöffnung >= 40x40cm
- Revisionsöffnung >= 60x60cm

Textergänzungen zu BMA

- x im Kanal
- DB im Doppelboden
- ZD in Zwischendecke
- H mit Signalmelder im Sockel
- Ex Explosionsgeschützt

1. 30cm mittig über OK Tür
2. 30cm mittig über OK Tür
3. 30cm unterhalb Decke
4. 30cm unterhalb Abhangdecke
5. Anbau an Decke (Aufbau)

Kennzeichnung Brandmeldeanlage

0/2/3 Melder-Nr.
- Meldergruppe Nr.
- Loop-Nr.

- RAS Anzuqöffnung Zwischendecke
- RAS Rohr Zwischendecke
- RAS Anzuqöffnung Decke
- RAS Rohr Decke
- RAS RAS Auswerteeinheit
- LWM-Fühlerrohr
- LWU LWM-Auswerteeinheit

Die Konformität der Bauteile nach DIN EN 54 sowie die Systemkonformität der BMA-Komponenten nach DIN EN 54/13 sind zu gewährleisten !

SAA

- Lautsprecher SAA
  - 1 LV Pos.5.2.1.20
  - 2 LV Pos.5.2.1.21
  - 3 LV Pos.5.2.1.22
  - 4 LV Pos.5.2.1.23
  - 5 LV Pos.5.2.1.25
  - 6 LV Pos.5.2.1.26
  - 7 LV Pos.5.2.1.27
  - 8 LV Pos.5.2.1.28

Türsprech-/Türöffneranlagen

- Türsprech-Videotableau
- Türsprech-Tableau
- Sprechstelle innen
- Sprechstelle innen System-Telefon
- Sprechstelle innen Video
- Klingeltaster
- BNG Busnetzgerät
- Läutwerk
- Türöffner

Lichtruf

- Notruf-Signalleuchte
- Ruf-Abstelltaster
- Zugtaster mit Schnur
- Zimmerterminal mit Display
- NGS Netzgerät USV
- I/O Modul
- Systemswitch

Übertragungsnetze

- Anschlußdose 1x/2x RJ45 Cat 6
- Festanschluss Cat 6
- Anschlußdose 2x LWL
- EV Etagenverteiler
- RV ZDV-Rangierverteiler
- Verteilerschrank 19"
- W.AN Wireless LAN Sende-/Empfangsstation
- DECT Sende-/Empfangsstation
- V.G.A VGA-Verbindungsdose
- HDMI HDMI-Verbindungsdose
- Audio Audio-Verbindungsdose

Kennzeichnung EDV-Anlage

1/2/3- Port-Nr.
- Patchfeld-Nr.
- Verteiler-Nr.

* = Ausstattung nach Vorgabe ELT nicht übereinstimmend mit Türliste Architekt Türdetail stimmt nicht!!! Klärung mit AG-Planern erforderlich

Grundkonzeption BOS-Gebäudefunk zur Zeit in Bearbeitung keine LP-5 vorhanden.

zur Zeit ausstehend Vorgaben der LP-5 zur Anbindung Türen/ RWA/ Entrauchung an die zentrale "Türsteuerung"

SAA-Hinweis: Die Lautsprechertypen nach Vorgabe LP-5 und LV sind nicht eindeutig zu zuordnen Klärung erforderlich!

Sprachalarmanlagen

- Amok Amok Taster oben
- Antenne
- Ton Eingang
- SAA Zentrale
- SAA-U Unterzentrale
- Festanschluss Lautsprecher
- Festanschluss Notruf
- Lautsprecher Anschlusspunkt
- Lautsprecher Anschlussdose
- Lautsprecher
- Lautstärke ELA
- Lautstärke Regler PFL-Relais
- Mikrofon SAA
- Sprechstelle SAA

Kennzeichnung Sprachalarmanlagen

1/2
- lfd. Nr.
- Linien-Nr.

Projektnummer	Gewerk	Lfdn	Planart	Ebene	Bauabschnitt	Freiheit	Index
K714	FIT	08	GR	03	Z3	1403	P00

Basispläne:
Architektur: ARCHITEKTUR
Ausführung: AUSFÜHRUNG

Übersicht:

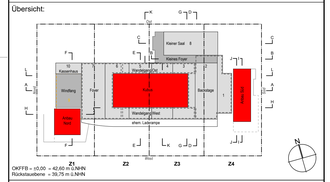

Bauvorhaben: KULTURRAFFINERIE K714 MONHEIM
Rheingarkallee 11
40789 Monheim am Rhein

Bauherr: Monheimer Kulturwerke GmbH
Am Kieswerk 4
40789 Monheim a. Rhein

Architekt: bez+kock architekten generalplaner gmbh
Königstr. 84
70173 Stuttgart

Fachplaner: ingenieurbüro fuhrmann + leuthen
beratende ingenieure für technisch Gebäudeausrüstung
gottlieb-daimler-straße 17
70567 stuttgart
tel. 0262-17264-0
info@ib-fuhrmann-leuthen.de
gravenbrucher 141
63263 neu-isenburg
tel. 0261-7594-220

Ausführende Firma: J.REHMS GEBÄUDETECHNIK
J. Rehms Gebäudetechnik GmbH • Siemensstraße 16
46325 Borken • T: 02861 / 9420-0 • F: 02861 / 9420-199
E-Mail: info@rehms-gmbh.de • www.rehms-gmbh.de

Projekt Nr.	FA050040	Leistungsphase	LPH-8
Maßstab	1:50	Planart	Grundriss
Blattgröße	1470x841	Etage/Ebene	3 Obergeschoss
Gezeichnet	06.12.2024 PW	Bauteil	Z3
Geprüft	06.12.2024 AW	Gewerk	FIT Grundriss
Datum	Name		

Projektnummer	Gewerk	Lfdn	Planart	Ebene	Bauabschnitt	Freiheit	Index
K714	FIT	08	GR	03	Z3	1403	P00